


- NOTAS:**
1. El presente plano modelo contempla acometida subterránea. En caso de ser necesario implementar una acometida aérea, se deben realizar los respectivos ajustes cumpliendo los requisitos del Capítulo 6. Título 26 del RETIE.
2. Los productos utilizados en la instalación eléctrica debe cumplir lo estipulado con el Título 2 del RETIE, teniendo en cuenta las condiciones medio ambientales presentadas en el municipio en el que se va a ejecutar el proyecto.

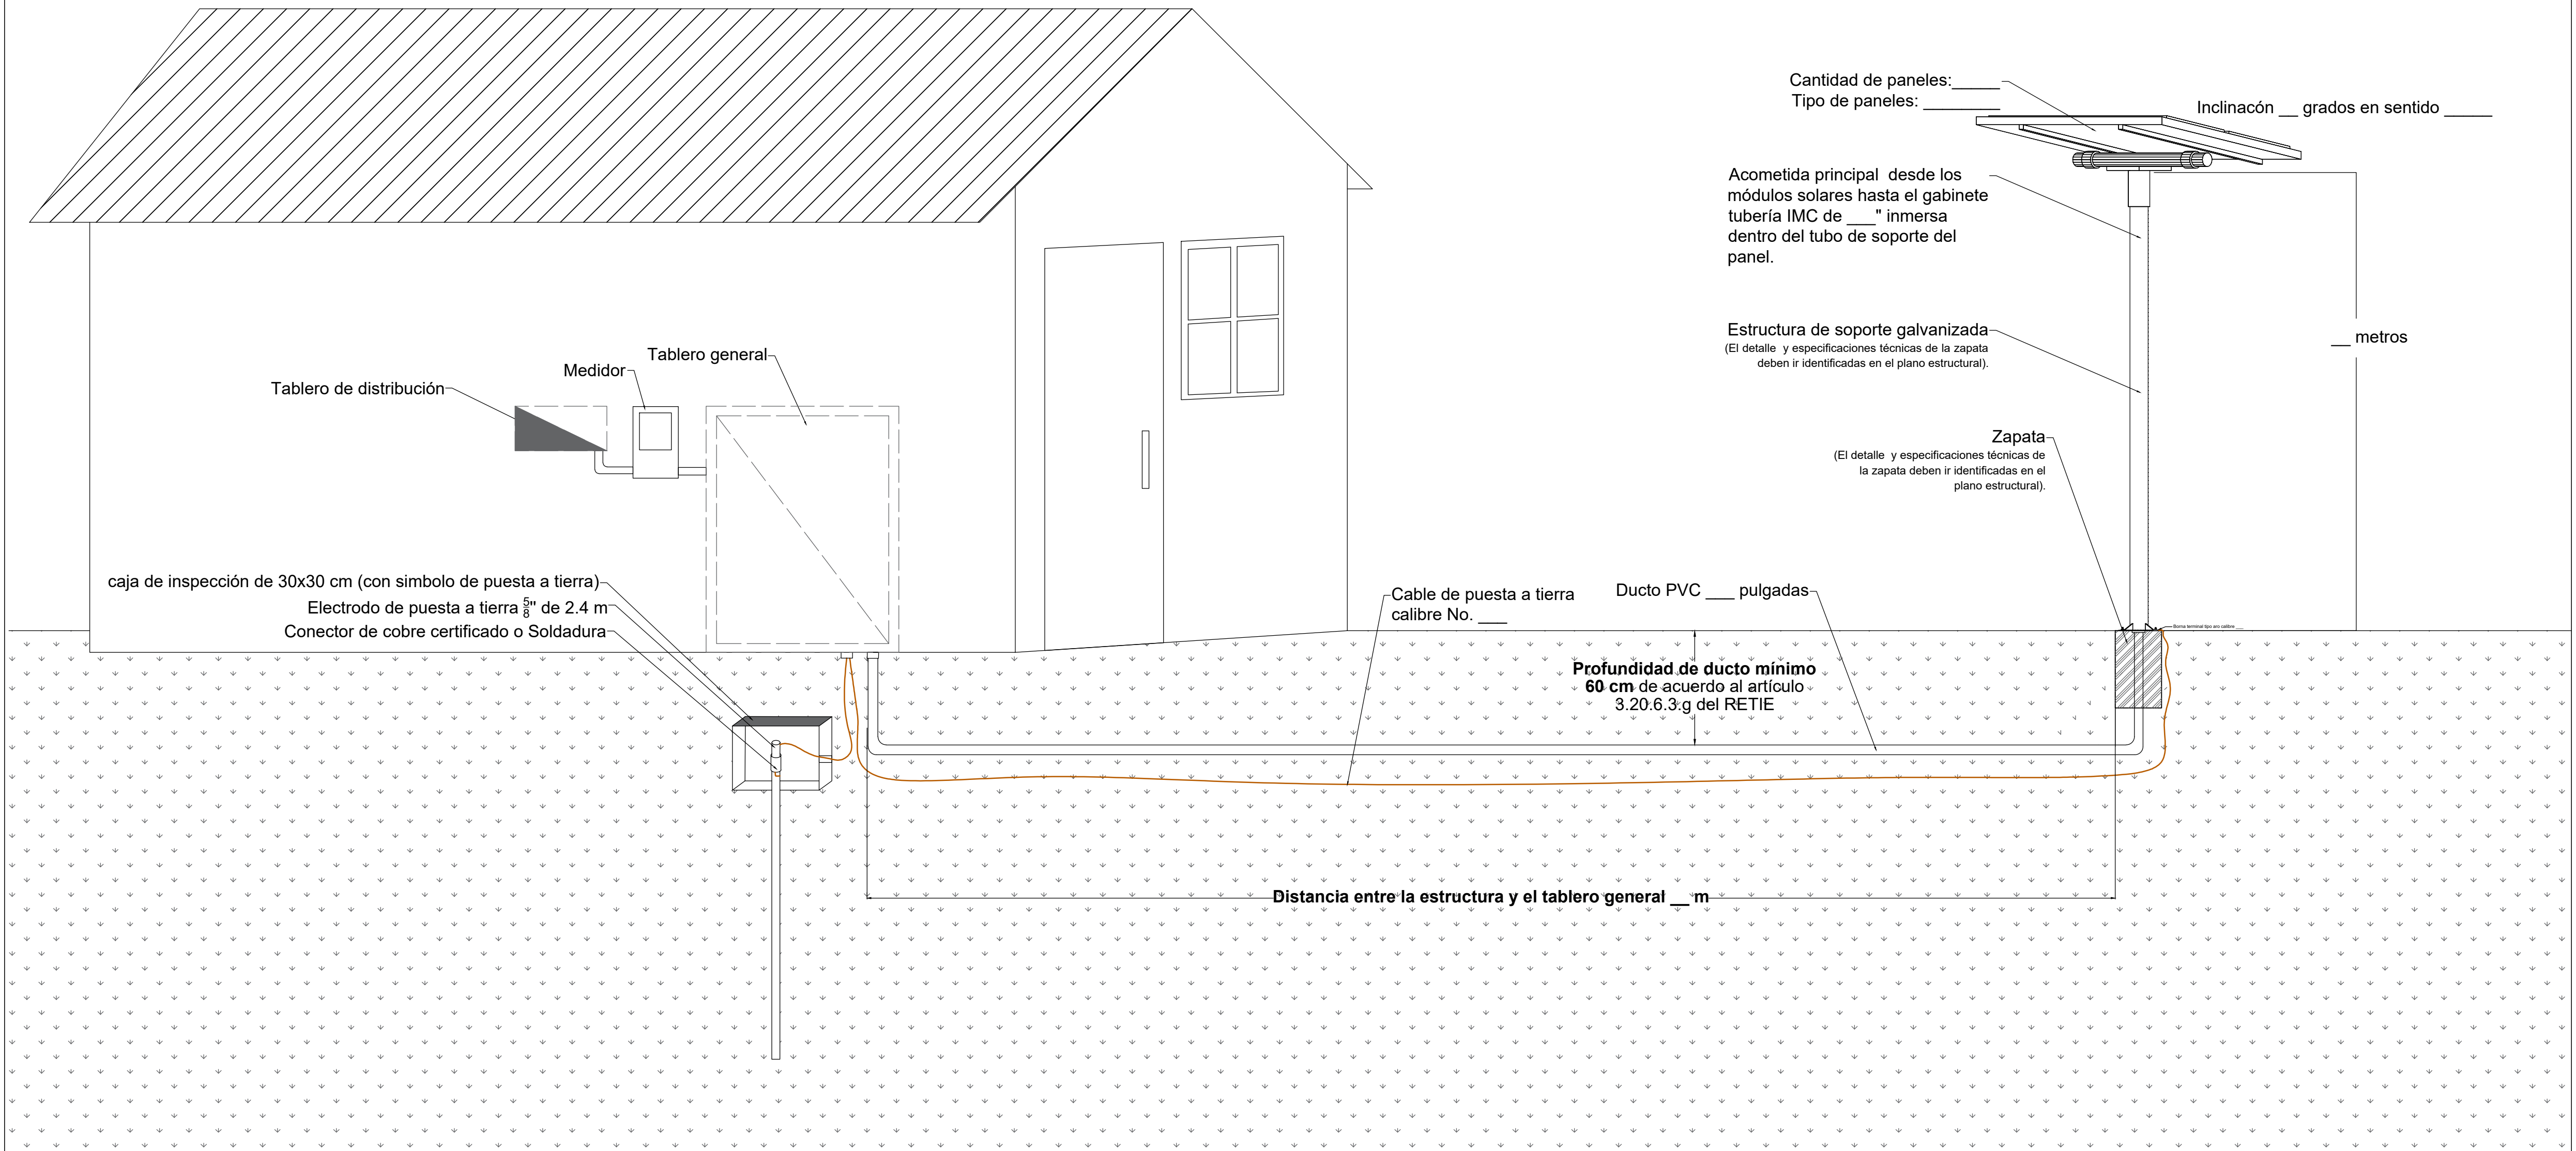

CONVENCIONES					LOGO-ENTIDAD	ENTIDAD QUE PRESENTA PROYECTO	LOCALIZACIÓN: PLANO DE LOCALIZACIÓN GENERAL DEL MUNICIPIO	CONTENIDO: ACOMETIDA ELÉCTRICA	BPIN: _____ PROYECTO: _____		
	Medidor		Tablero de distribución (interior de la vivienda)						“ _____ ”		
	Tablero general (interior de la vivienda)										
								PRESENTO: _____ (Nombre del ingeniero) Ingeniero Electricista M.P.: __205-_____	DISEÑO: _____	REVISO: _____	
									APROBÓ: _____	FECHA: _____	
									DIBUJO: _____	Plano 1/____	Escala: Predeterminada