
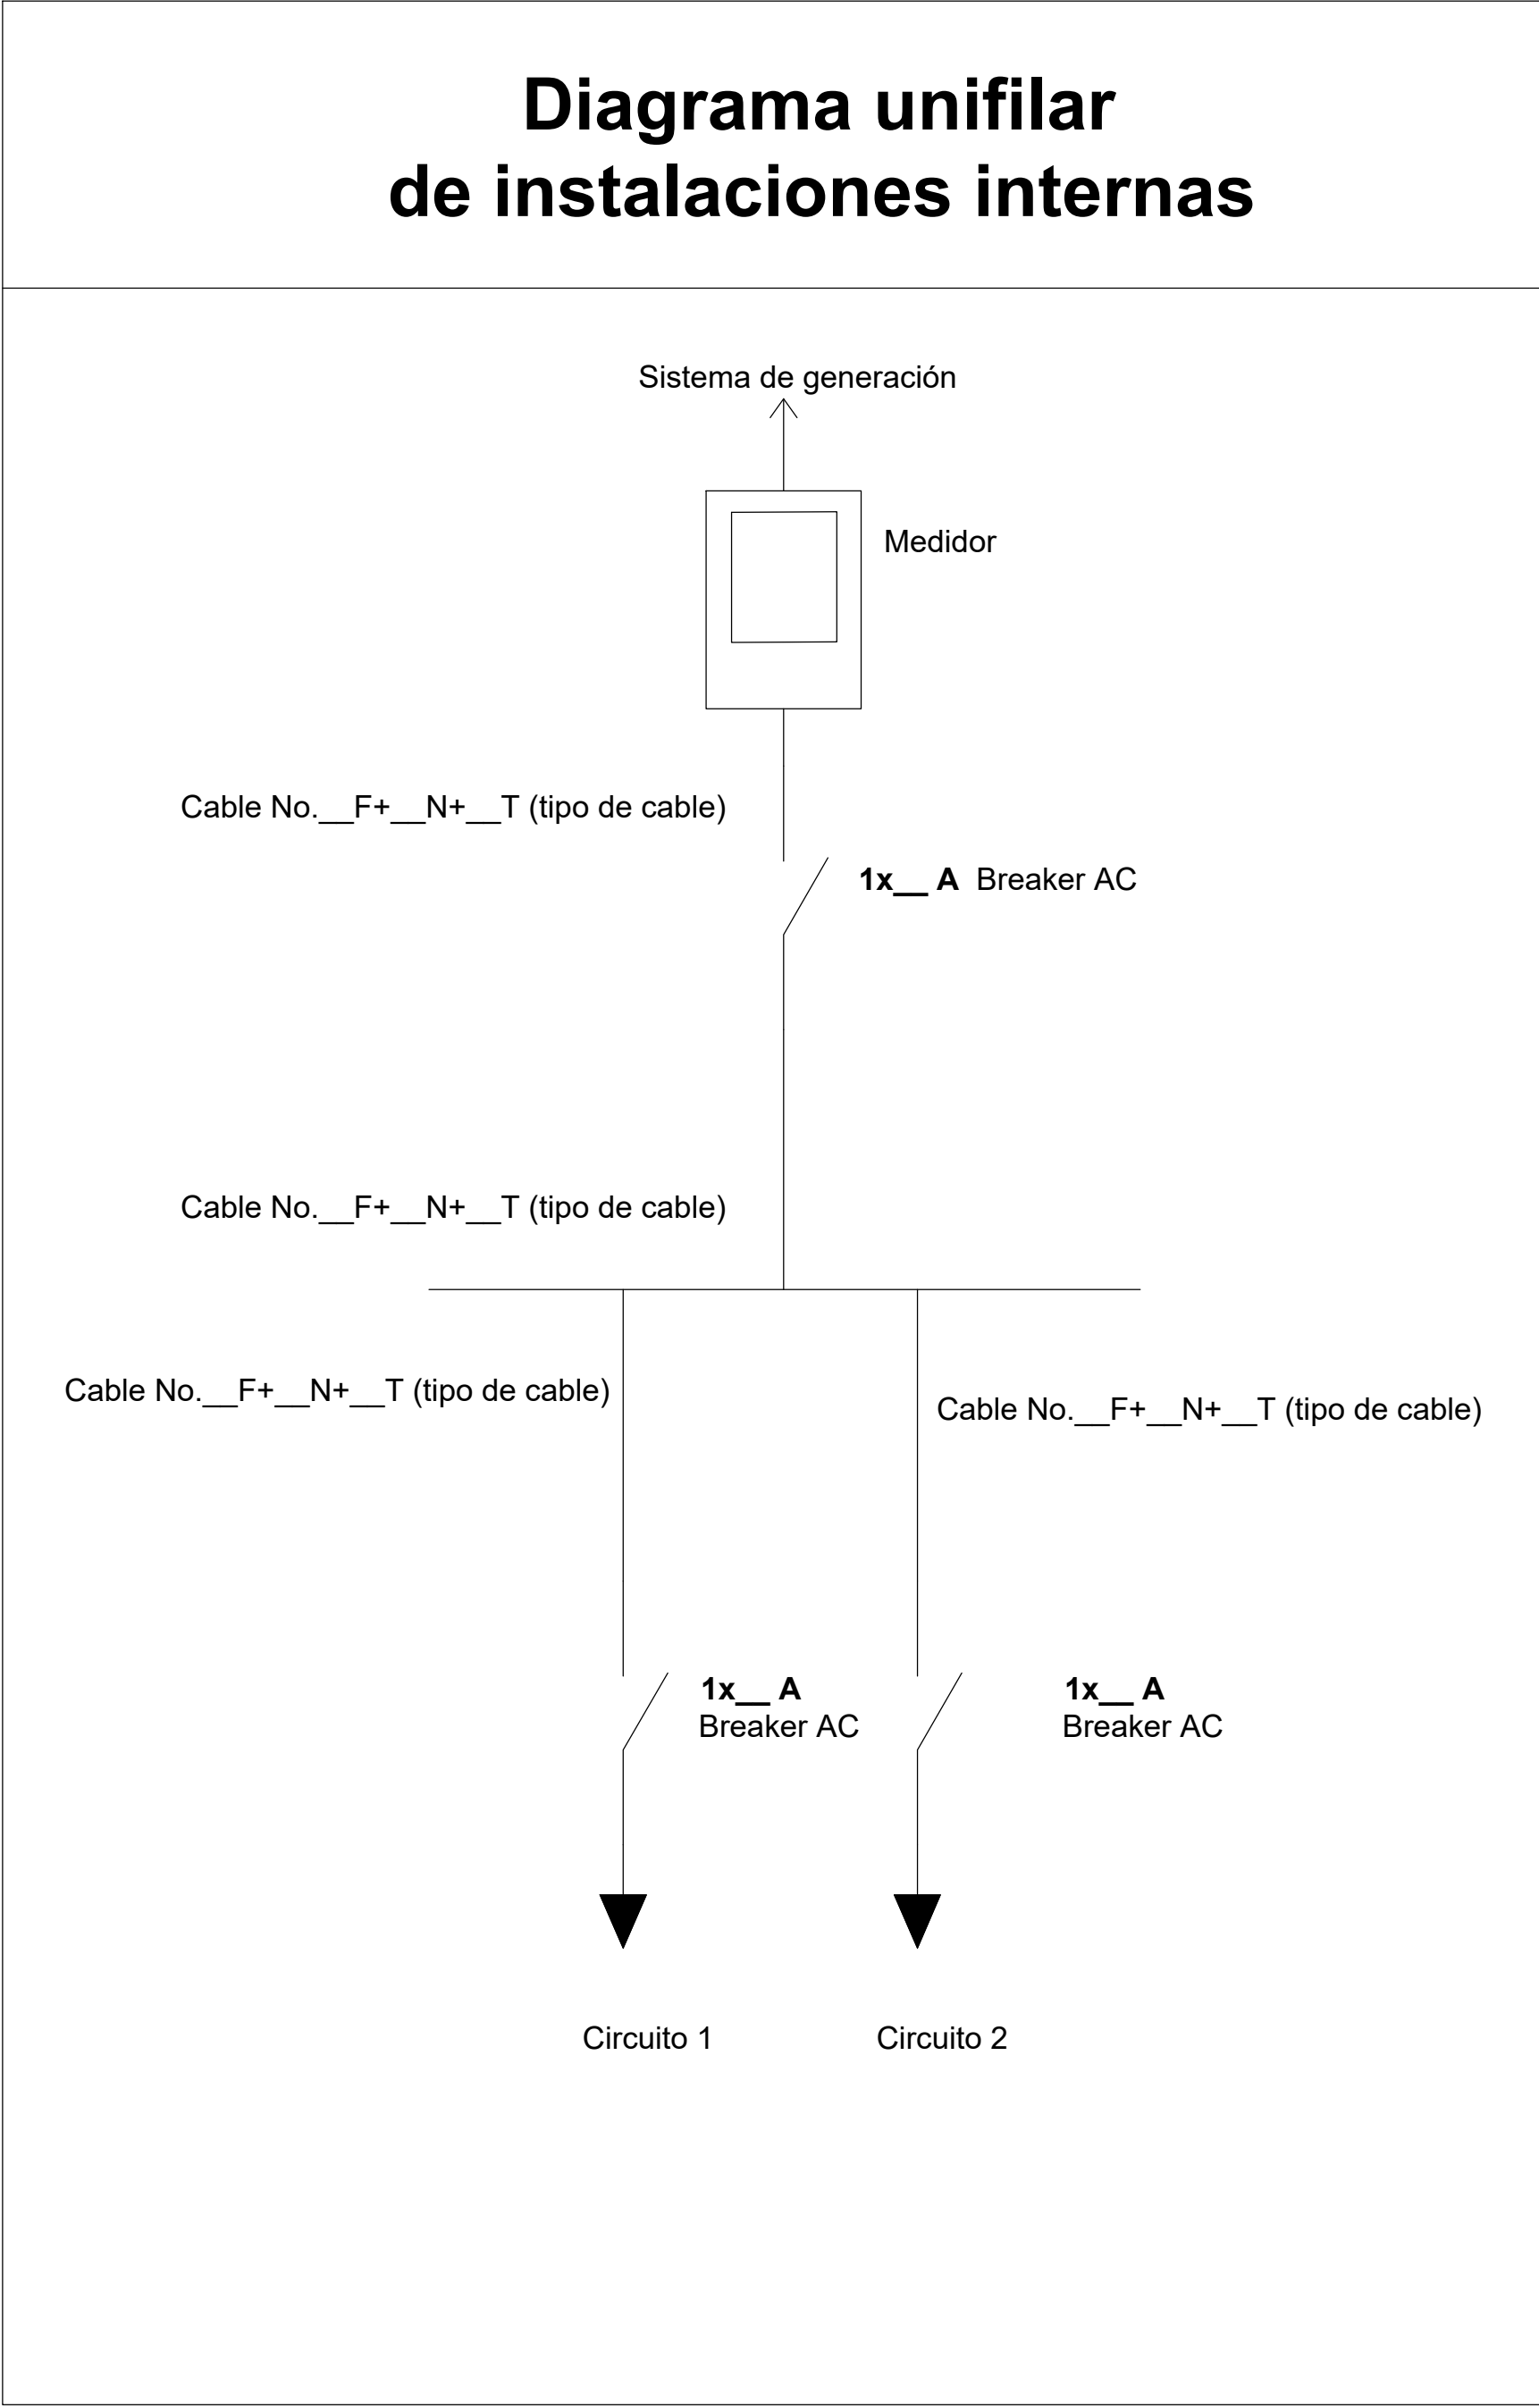


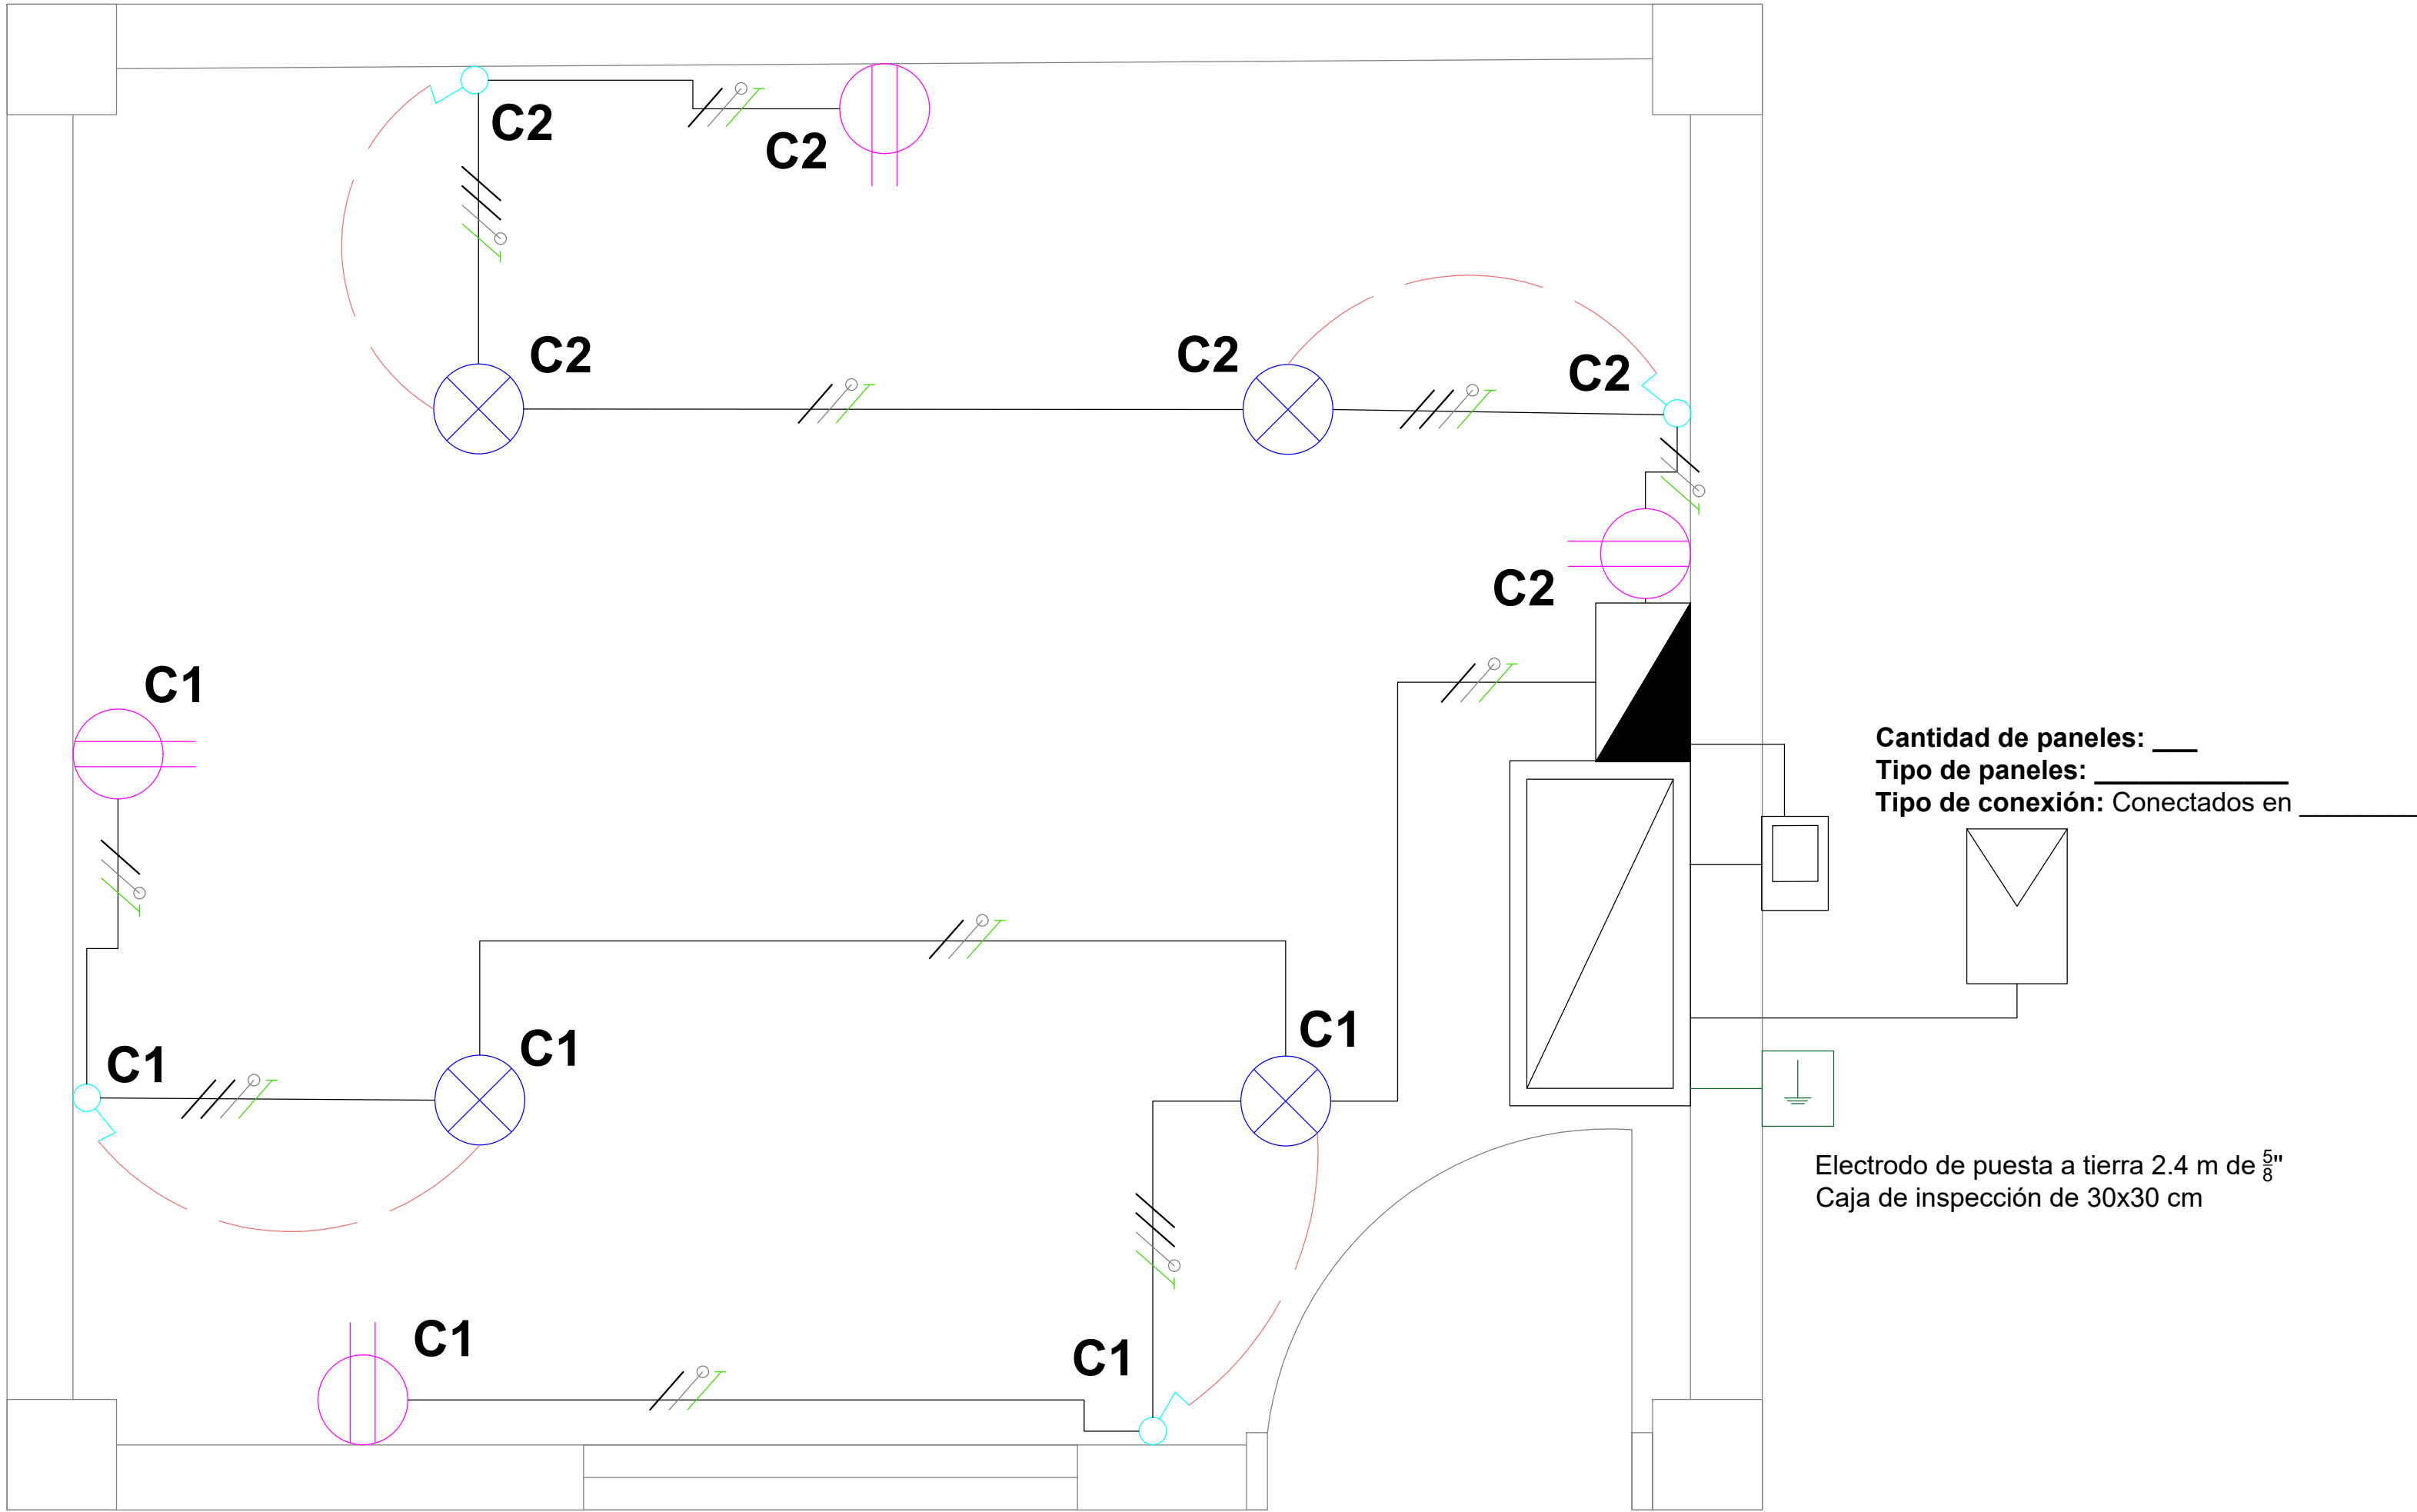

- NOTAS:**
- 1. Se debe realizar las respectivas conexiones equipotenciales en cada elemento metálico que aloje equipo eléctrico de acuerdo a la sección 250.V de la NTC 2050.
 - 2. Se instalará tubería tipo _____ de _____ pulgadas.
 - 3. Se instalarán contuctores tipo _____ calibre _____ para fase, neutro y tierra respectivamente.

CONVENCIONES					LOGO-ENTIDAD	ENTIDAD QUE PRESENTA PROYECTO	LOCALIZACIÓN: PLANO DE LOCALIZACIÓN GENERAL DEL MUNICIPIO	CONTENIDO: INSTALACIONES INTERNAS “	BPIN: _____ PROYECTO: _____					
	Sistema de generación		Tablero de distribución	C1					Circuito 1					
	Tomacorriente monofásico		Interruptor sencillo	C2					Circuito 2					
	Salida de iluminación		Tablero general						Conductor de Fase					
	Circuito		Protección						Conductor de Neutro					
	Sistema de puesta a tierra		Caja de medidor						Conductor de Tierra					
									PRESENTO:		DISEÑO: _____		REVISO: _____	
									(Nombre del ingeniero) Ingeniero Electricista M.P: __205-_____		APROBÓ: _____		FECHA: _____	
											DIBUJO: _____		Plano 1/ __	Escala: Predeter