



DIAGRAMA UNIFILAR

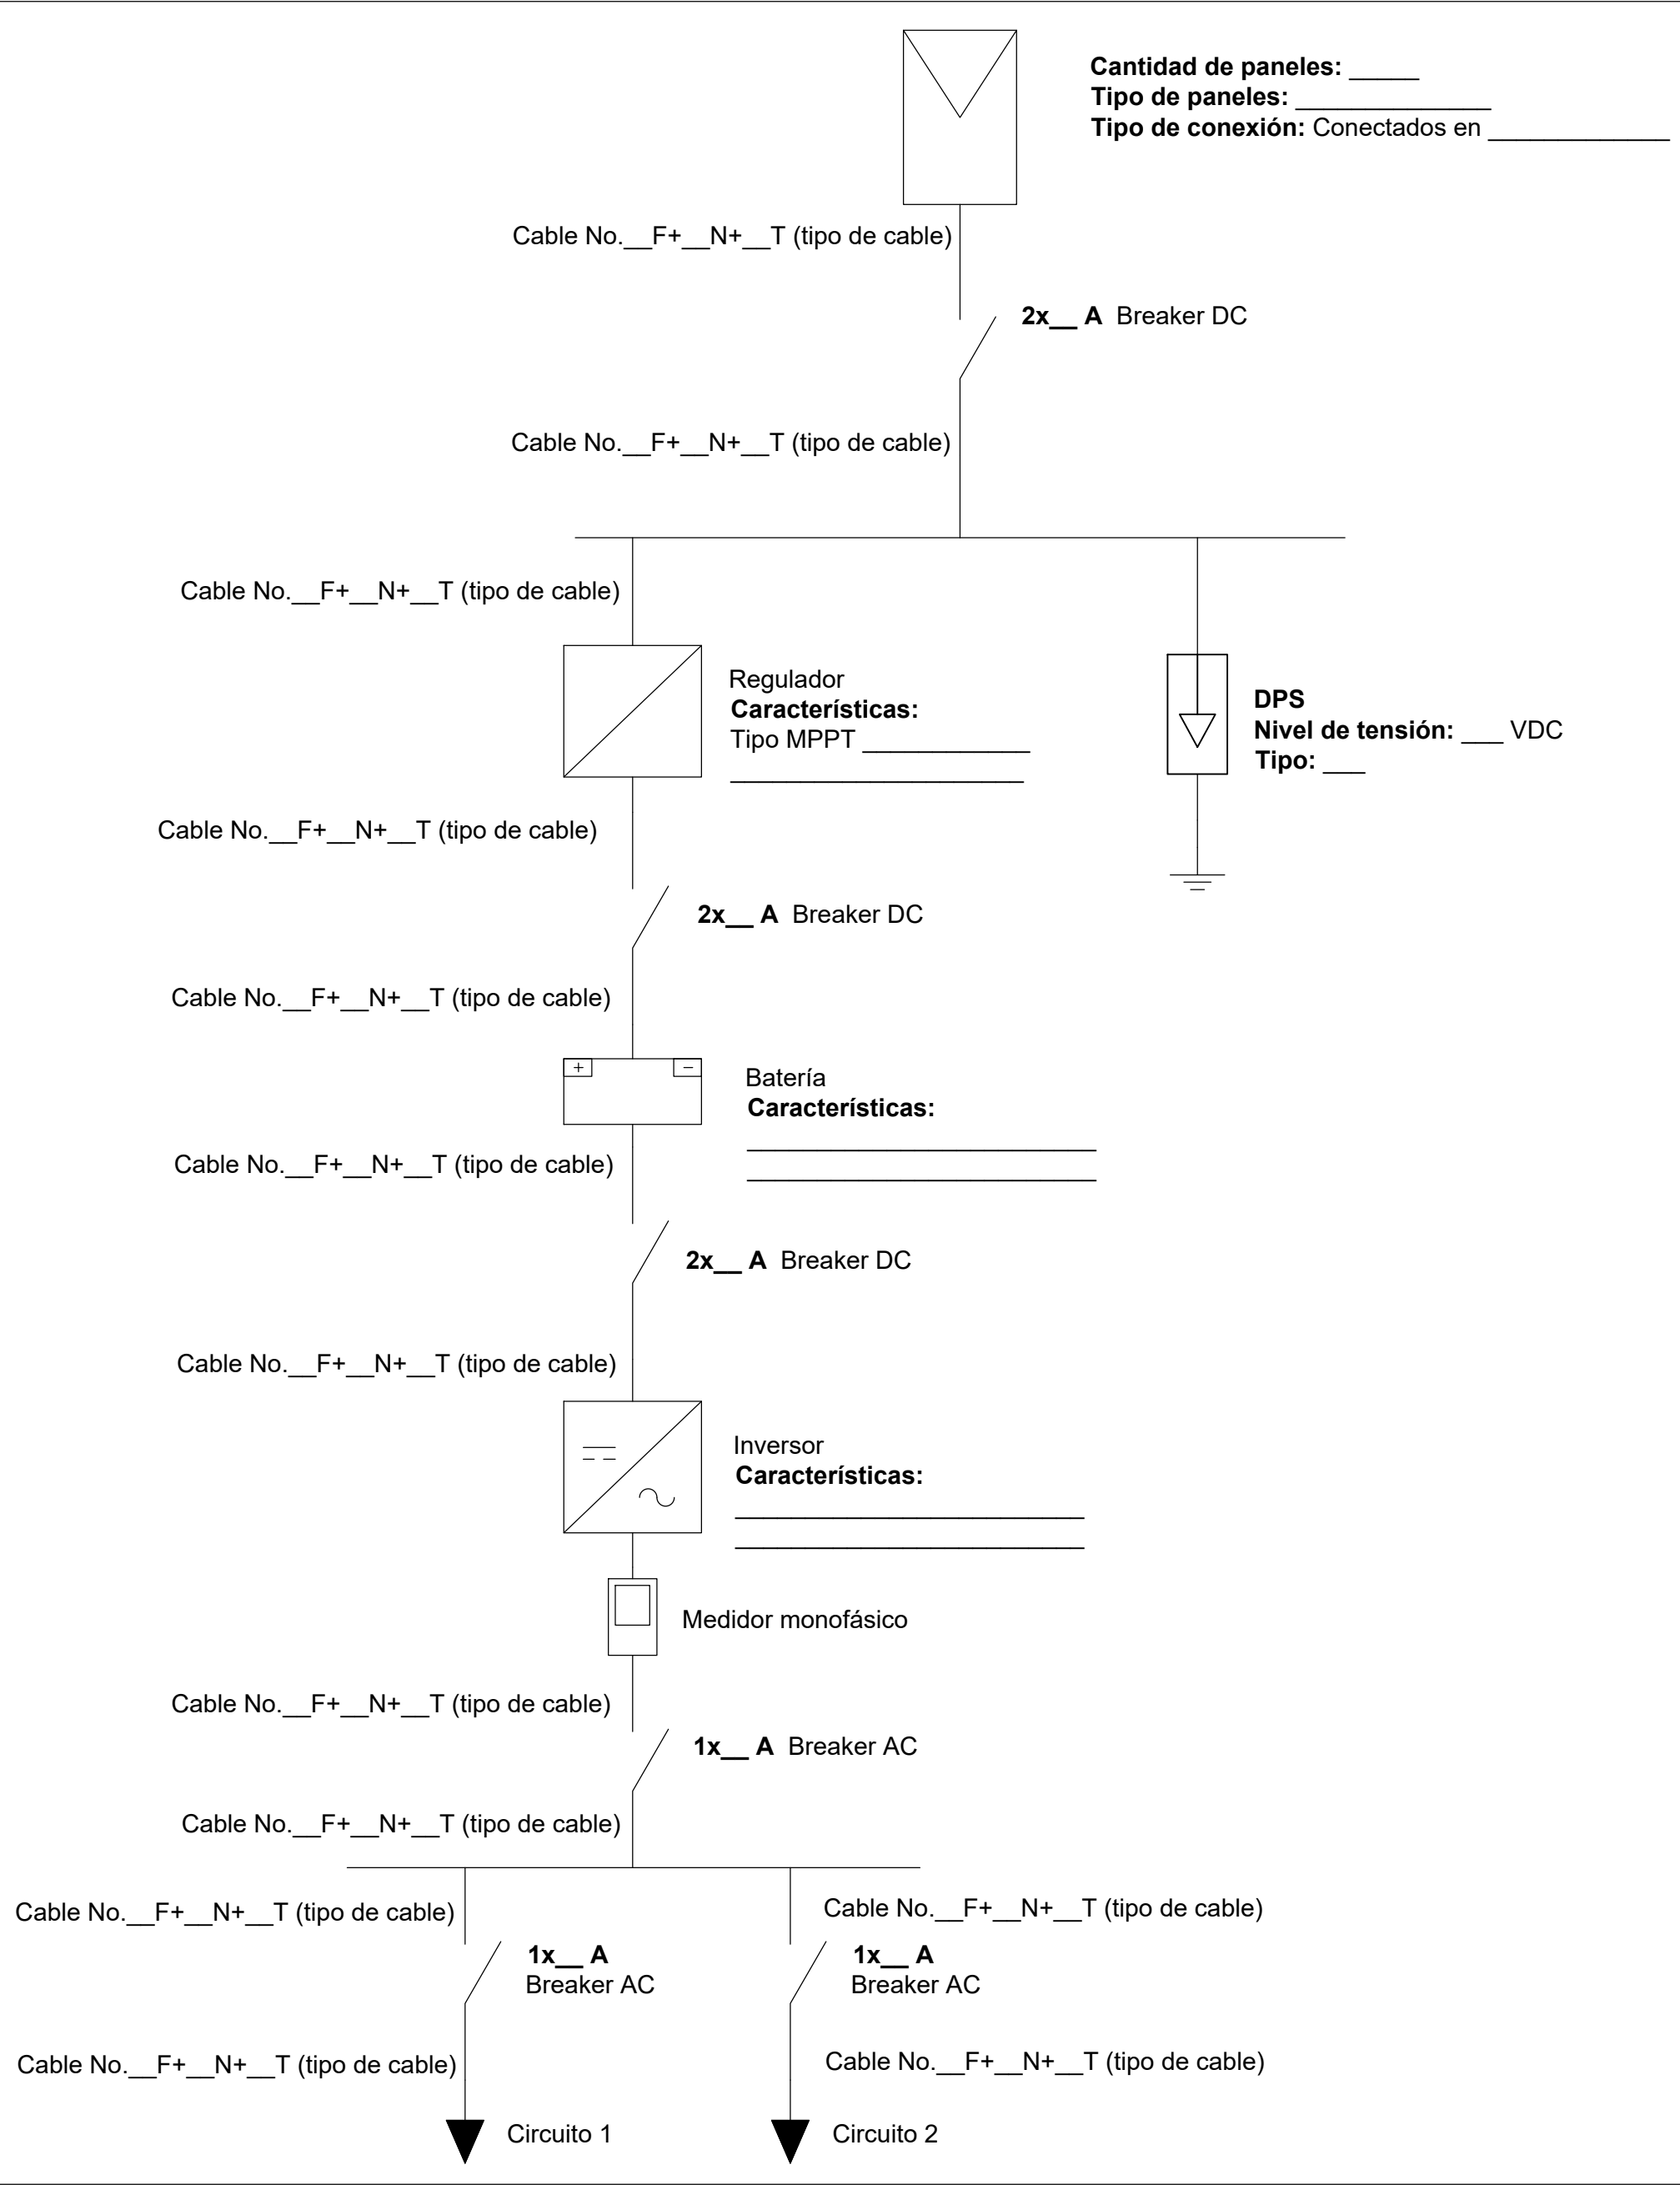

ESQUEMA DE CONEXIÓN

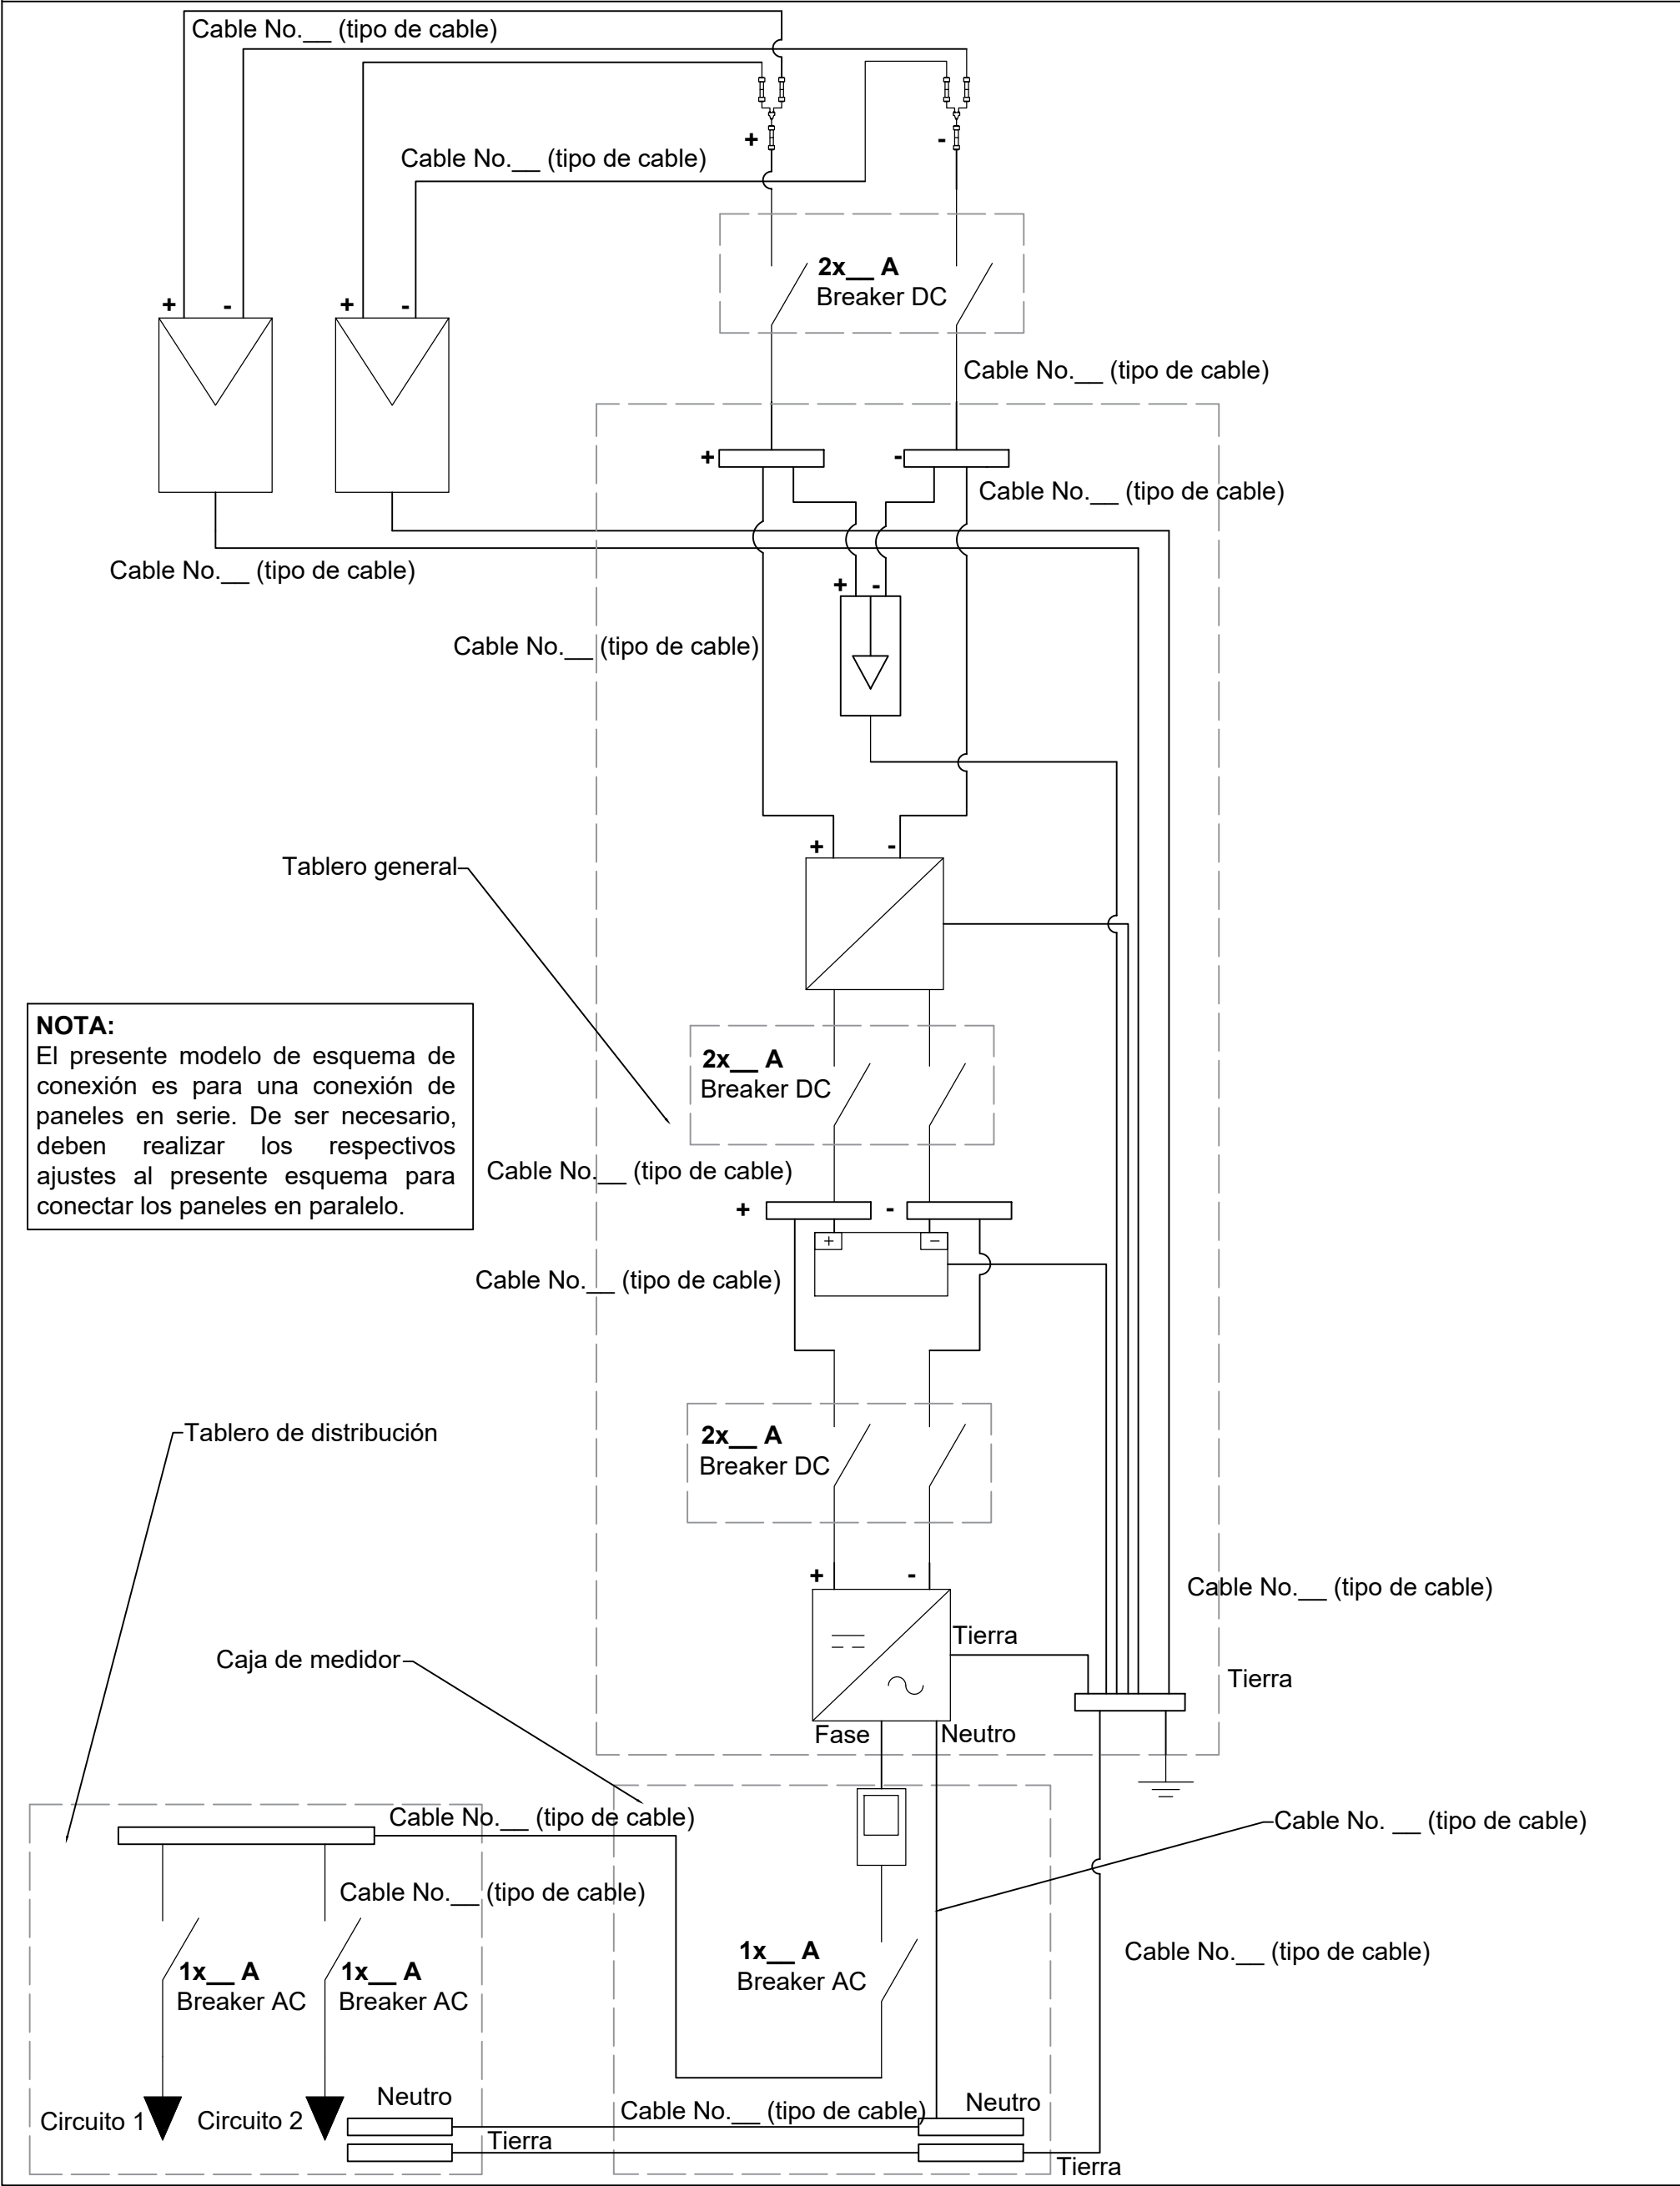

CONVENCIONES

	Sistema de generación		Inversor		
	DPS		Batería		
	Circuito		Regulador		
	Medidor monofásico		Protección		
	Sistema de puesta a tierra		Conector		

LOGO-ENTIDAD

ENTIDAD QUE
PRESENTA
PROYECTO

LOCALIZACIÓN:

PLANO DE
LOCALIZACIÓN
GENERAL DEL
MUNICIPIO

CONTENIDO:

DIAGRAMA UNIFILAR
Y
ESQUEMA DE CONEXIÓN

PRESENTO:

(Nombre del ingeniero)
Ingeniero Electricista
M.P.: __205-__

BPIN: ____
PROYECTO: ____

DISEÑO: ____ REVISO: ____

APROBÓ: ____ FECHA: ____

DIBUJO: ____ Plano 1/____ Escala: Predeter